

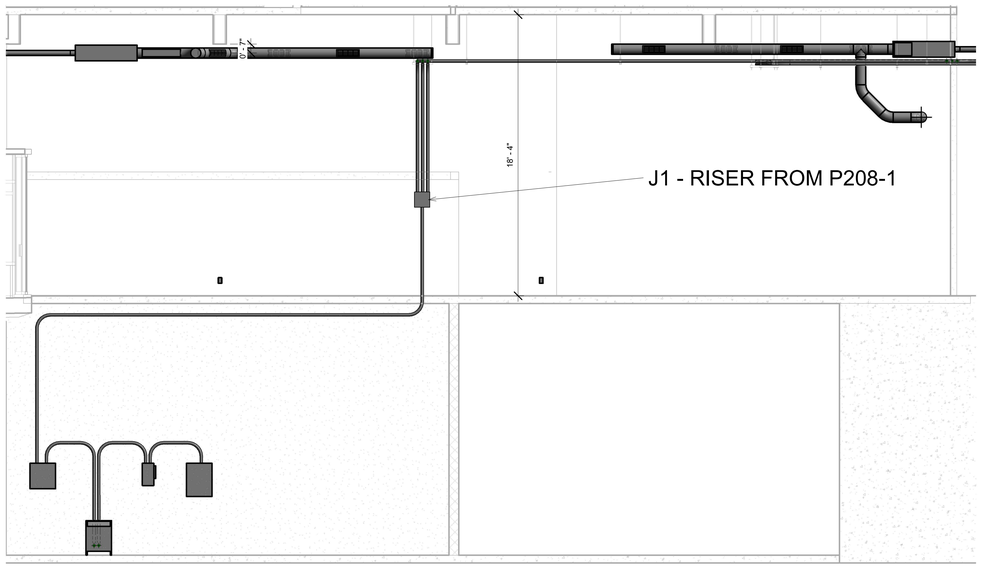



2 Retail 109 - Raceway Coordination
1/4" = 1'-0"

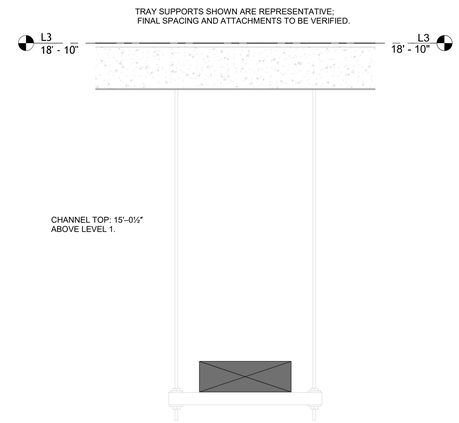

5 Retail 109 - Typical Cable Tray Detail
1 1/2" = 1'-0"

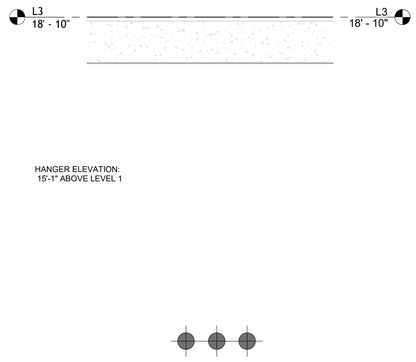


1 Retail 109 - Typical Conduit Rack Detail
1 1/2" = 1'-0"

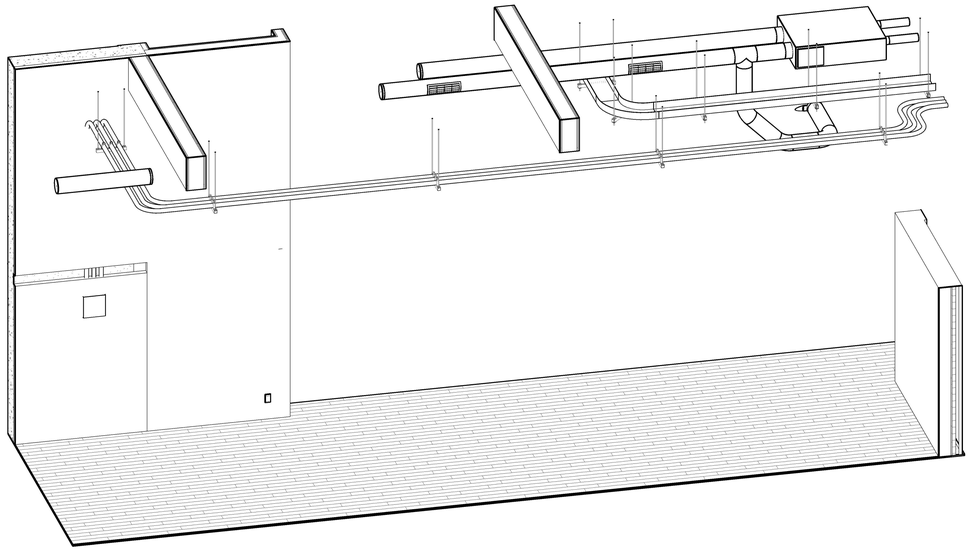

3 3D - L1 - Retail 109

CONDUIT & CABLE TRAY CONTINUE BEYOND MODEL SCOPE.
SUPPORTS BEYOND THIS POINT NOT SHOWN

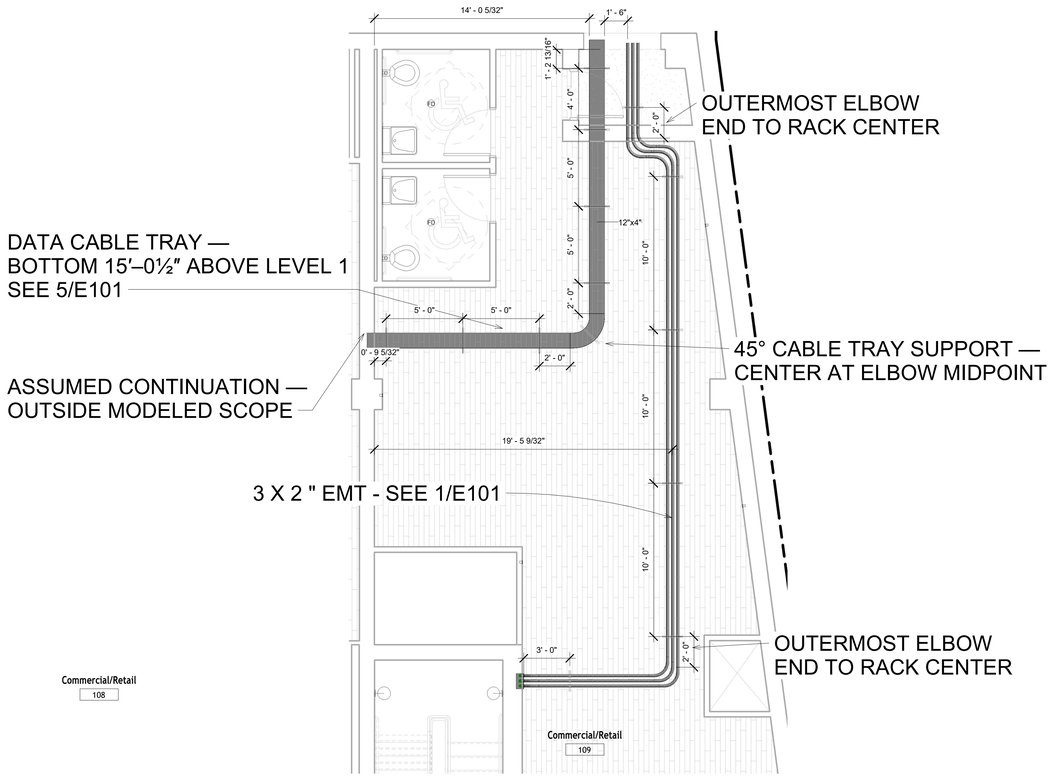

4 Retail 109 - Raceway Plan
1/4" = 1'-0"

INDEPENDENT EDUCATIONAL PROJECT — NOT FOR CONSTRUCTION

www.autodesk.com/revit

Consultant
Address
Address
Address
Phone

Consultant
Address
Address
Address
Phone

Consultant
Address
Address
Address
Phone

Consultant
Address
Address
Address
Phone

Consultant
Address
Address
Address
Phone

No.	Description	Date

Isaak Meakin

ST Electrical

Retail 109 - Raceways

Project Number	ST-001
Date	10/8/26
Drawn By	Isaak Meakin
Checked By	Checker

E101

Scale	As indicated

10/14/2026 12:17:31 AM